Staging level framing plan (-15), as built, deck removed

Looking down. Orange = L-girders (1x4 web + 1x2 flange); tan = 1x3 joists.

Dimensions in inches. 0.00 = top of 3/4 ply subroadbed (0" grade).

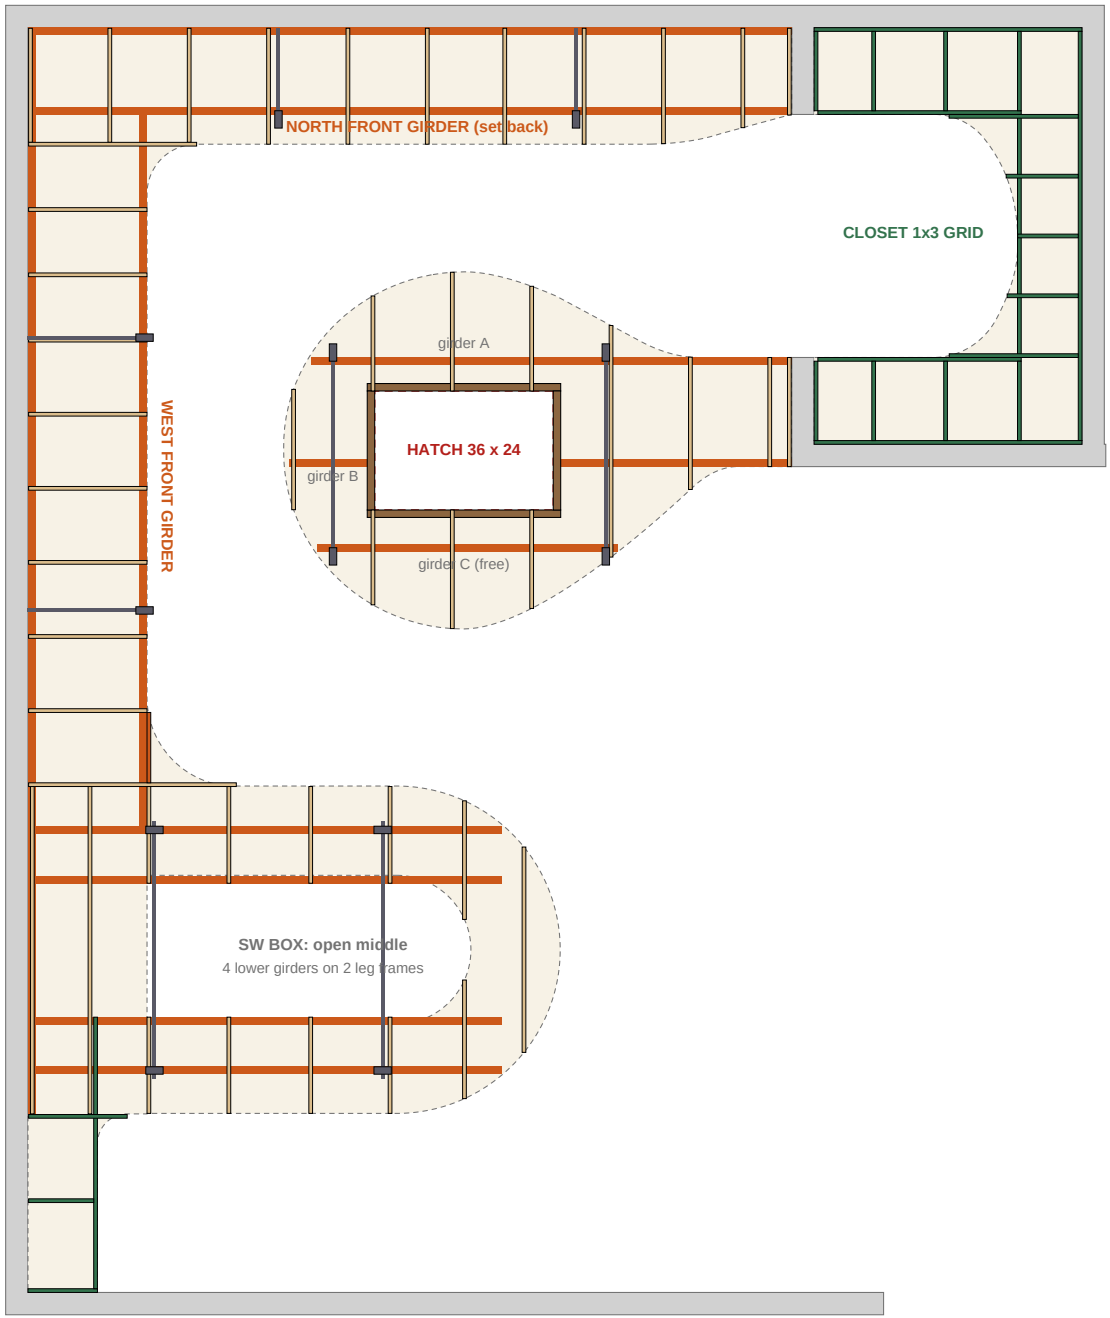

LEGEND

- L-girder, 1x4 web + 1x2 flange (wall, front, SW, helix)
- 1x3 joist, ~16 in o.c.
- 2x4 leg / 1x4 leg-frame joist
- 2x4 hatch frame
- Closet 1x3 grid (as the main level)

NOTES

Deck top -15, 3/4 ply on 1x3 joists sitting straight on the girder flanges (flange top -18.22). Same outlines and seams as the 0 in level, so the joist stations on the wall runs are the main level's.

Legs: 2x4 legs under a 1x4 joist that carries the girders, 1x2 diagonals on every leg. Two frames on the north run and two on the west run (wall girder to front girder); two on the SW box, under the west and east straights, each carrying all four lower girders.

SW box: upper girders (y 218-1/2, 248-1/2) carry the main level; the lower inner pair sits under them, the outer pair 10 in further out. Deck: two 18 in straights and a solid bullnose round the tip; the middle is open.

Helix peninsula: girders A and B come off the closet wall on the neck edges and run to the bulb's west edge; B is cut out at the hatch. C is free, halfway to the south edge. A 2x4 + 1x4 leg frame carries all three at each end.

TO VERIFY ON SITE

- Girder lines on the wall runs (drawn like the main level: north set back to y 65, west under the edge).
- Leg frame positions: north run x 55, 115; west run y 110, 165; SW box x 30, 76; helix x 66, 121.
- Hatch size and position (placeholder 36 x 24 on the helix centre); girder y positions A, B, C.
- SW girder ends (drawn to x 100) and where the west front girder ends (drawn onto the outer SW girder).
- FG / GG / bullnose seam lines (drawn at the loop centre, x 78.8).

Room inches: x east from the west wall corner, y south from the north wall line (same as the main level). Plan about 1:39.

Staging level sections

A: wall run (west). B: SW box, north-south at x 60. C: helix peninsula, north-south through the hatch.

Dimensions in inches. 0.00 = top of 3/4 ply subroadbed (0" grade).

A WALL RUN (WEST) 1:10

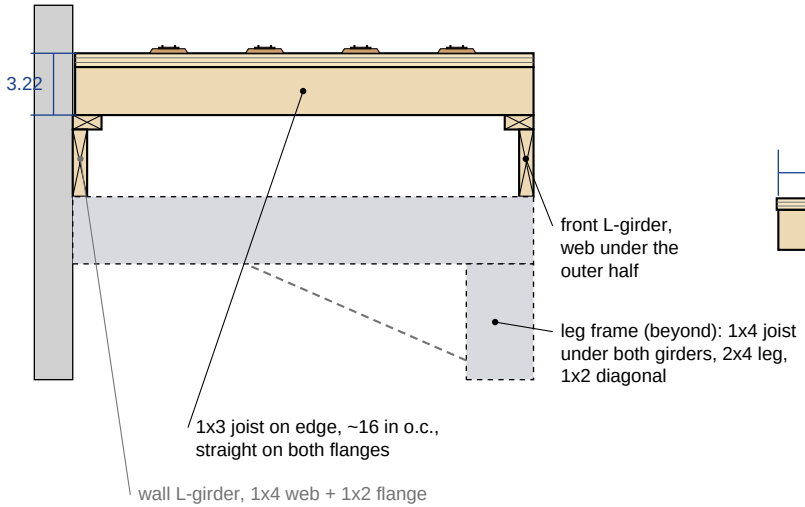

B SW BOX, NORTH-SOUTH AT x 60 1:12

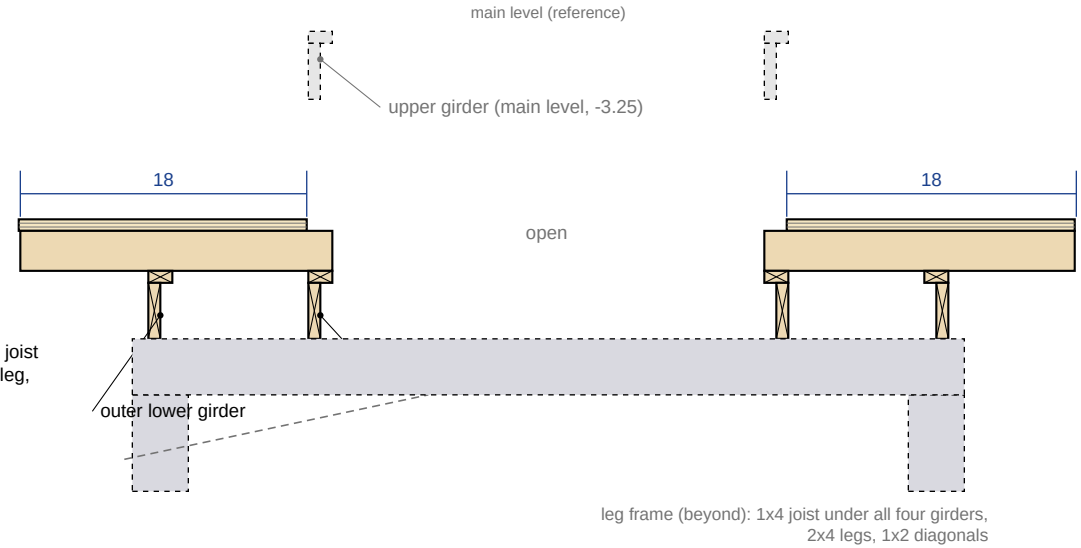

C HELIX PENINSULA, NORTH-SOUTH AT x 92 (THROUGH THE HATCH) 1:10

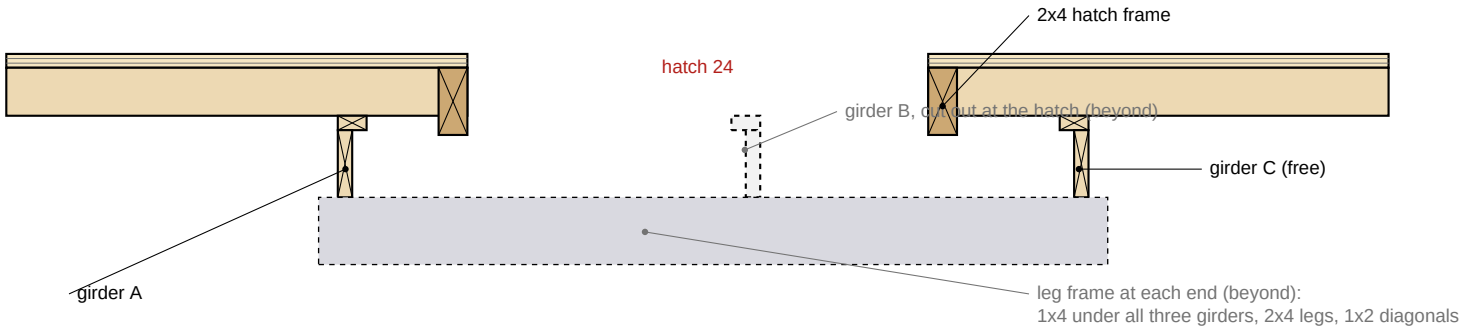

Elevations: deck top -15.00; joist top -15.72, bottom -18.22 = girder flange top; web bottom -22.47. Floor not measured. Dashed grey = main level, legs and parts beyond the cut.

Staging level plywood pieces (3/4)

As the 0 in level except the SW box (two 18 in straights + a solid bullnose) and B2/B3 through the closet wall.

Dimensions in inches. 0.00 = top of 3/4 ply subroadbed (0" grade).

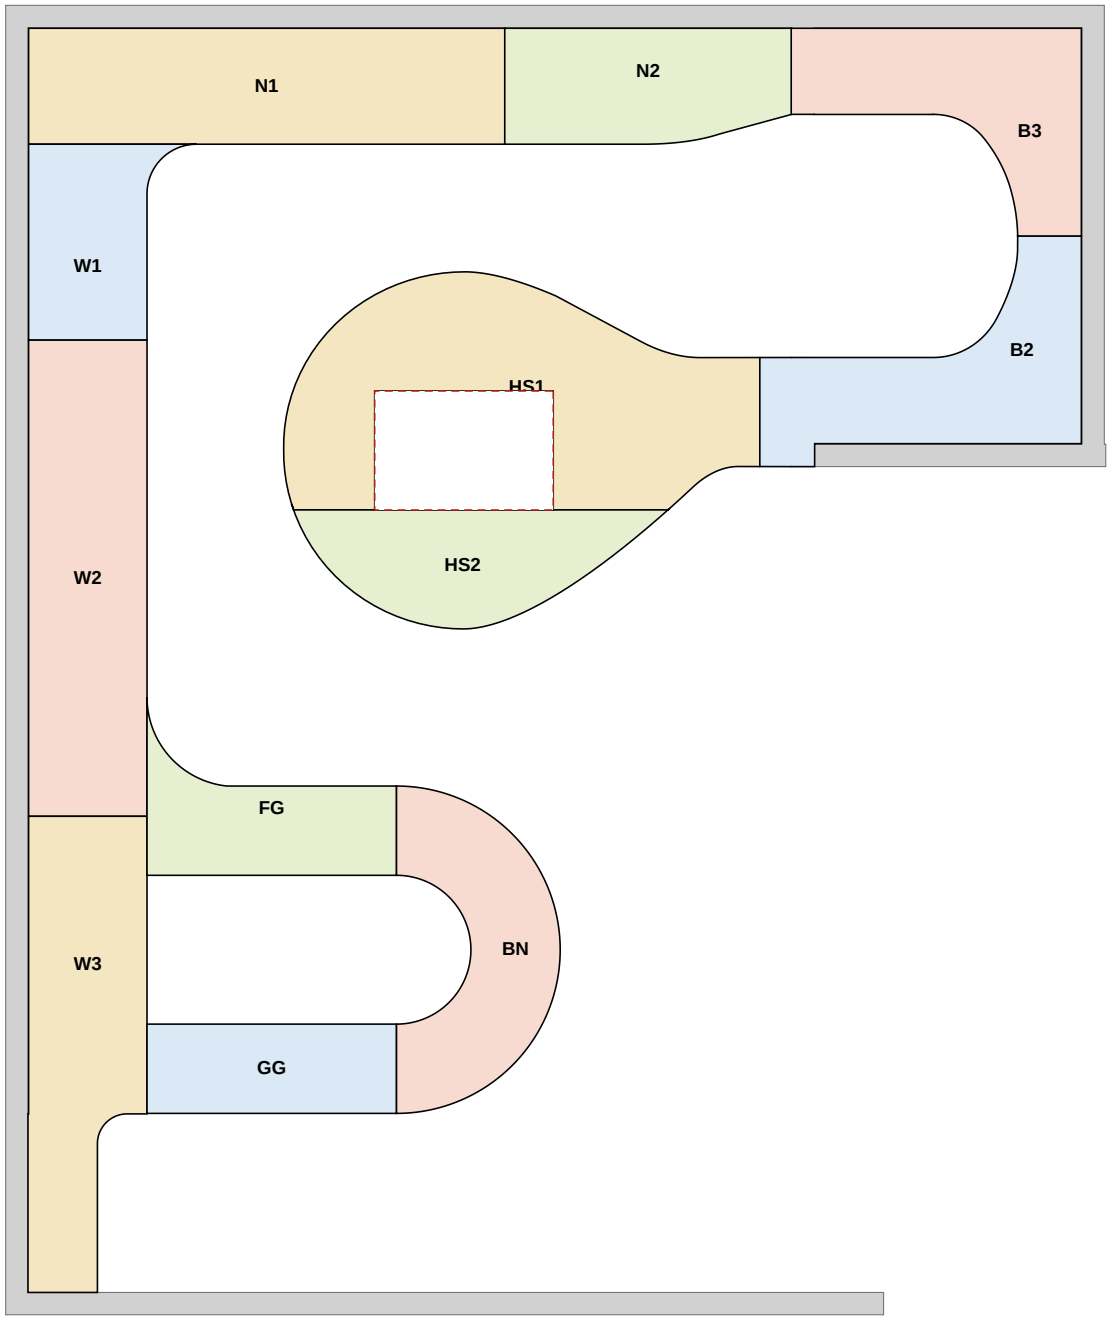

PIECE	WHERE	BOUNDING (E-W x N-S)
N1	North wall square cuts	96 x 23-3/8
N2	North wall east eased front edge	57-7/8 x 23-3/8
W1	West wall, north end with the 10 in NW fillet	33-7/8 x 39-1/2
W2	West wall, middle 96 in	23-7/8 x 96
W3	West wall south end + closet strip 96 in	24 x 96
FG	SW box, north straight 18 in rectangle + the F3 fillet curve	50-1/4 x 35-7/8
GG	SW box, south straight 18 in rectangle	50-1/4 x 18
BN	SW box, bullnose (G2 + G3) one solid piece round the tip	33 x 66
HS1	Helix peninsula, north full 48 x 96 sheet, bulb to neck	96 x 48
HS2	Helix peninsula, south span around the hatch	76-1/4 x 25-1/4
B2	Closet deck, south half through the wall to HS1 (takes the neck end)	64-7/8 x 46-1/2
B3	Closet deck, north half through the wall to N2	58-1/2 x 41-7/8

Pieces mirror the main-level cut plan; edges are the AnyRail outlines. Dashed red = hatch. Sizes are bounding boxes, not cut dimensions.