

← WEST EAST →


STAGING LEVEL

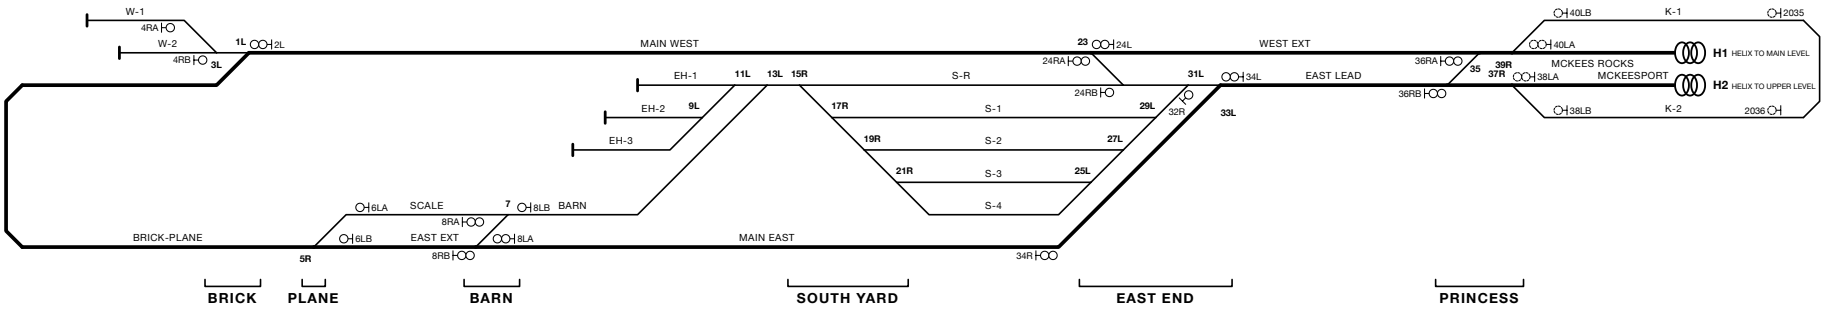

MAIN LEVEL

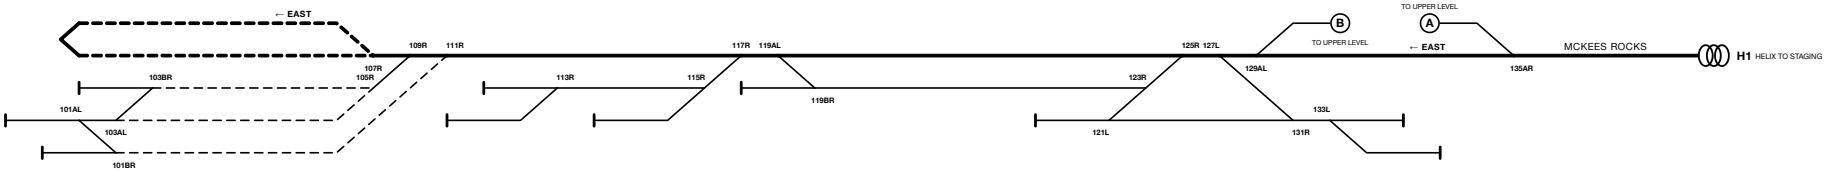

UPPER LEVEL, 4.25 IN

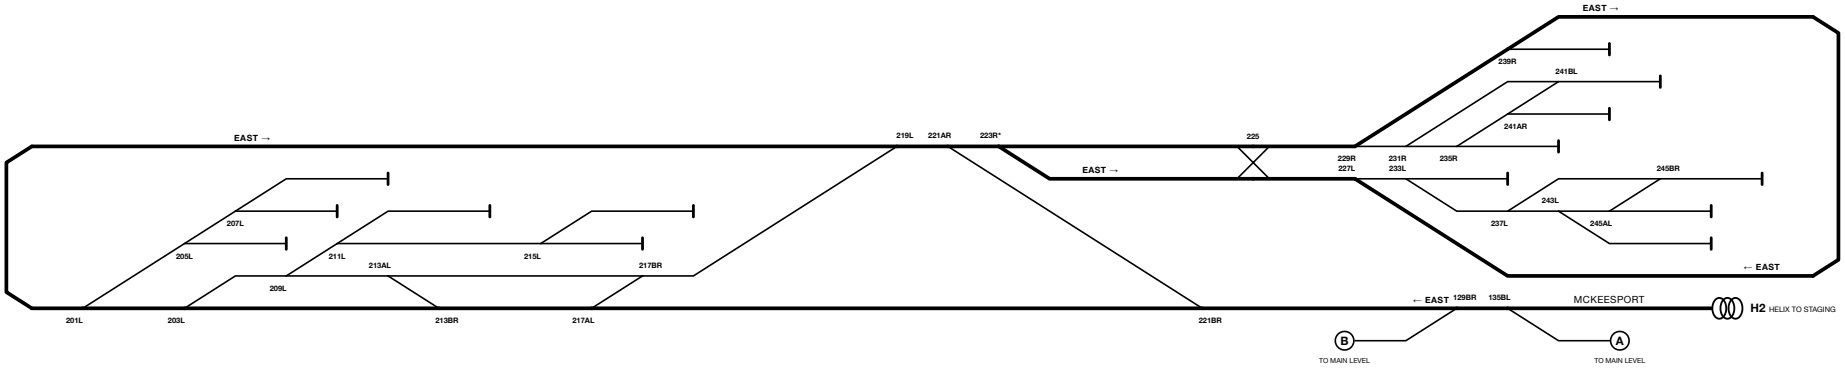

SYSTEM SCHEMATIC STAGING, MAIN AND UPPER LEVEL STAGE 0 PROOF, AS BUILT **DRAFT**	NOV 14, 2026 REV 3 SHEET 1 OF 1